


DESCRIPTION AS FURNISHED: Lot 431, TRINITY LAKES PHASE 3, as recorded in Plat Book 80, Pages 47 through 54 of the Public Records of Lake County, Florida.

PLOT PLAN FOR/CERTIFIED TO: Landsea Homes

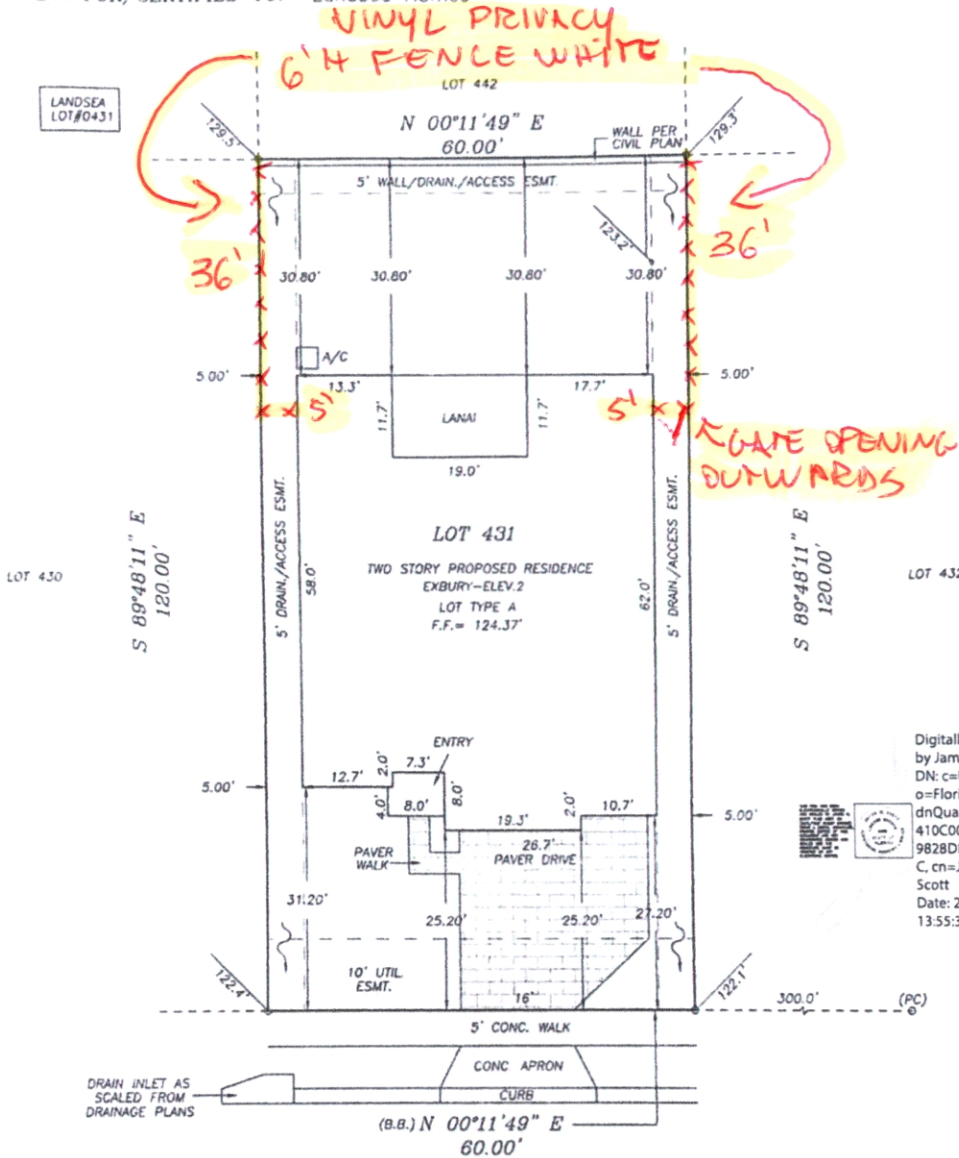

Digitally signed
by James W Scott
DN: c=US,
o=Florida,
dnQualifier=A01
410C0000185B6
9828DF00120A6
C, cn=James W
Scott
Date: 2024.03.14
13:55:30 -04'00'

DILLY LAKE AVENUE
(50' R/W)

BUILDING SETBACKS: (AS FURNISHED)
FRONT = 25' (FRONT LOAD GARAGE)
FRONT = 15' (ANY OTHER STRUCTURE/PORCH)
REAR = 10' (5' FOR POOL & POOL DECK)
SIDE = 5'
CORNER SIDE = 15'

PROPOSED = FINISHED SPOT GRADE ELEVATIONS
PER DRAINAGE PLANS

~ = PROPOSED DRAINAGE FLOW

DRAINAGE TYPE A

PROPOSED FINISH FLOOR PER PLANS = 124.37'


PLOT PLAN ONLY NOT A SURVEY

PLOT PLAN AREA CALCULATIONS
IMPERVIOUS COVERAGE = 3,773± SQUARE FEET OR 52.4%
LOT CONTAINS 7,200± SQUARE FEET

GRUSENMEYER-SCOTT & ASSOC., INC. - LAND SURVEYORS

LEGEND -
P = PLAT
F = FIELD
I.P. = IRON PIPE
I.R. = IRON ROD
C.M. = CONCRETE MONUMENT
SET I.R. = 1/8" I.R. w/RLB 4546
REC = RECOVERED
P.B.S. = POINT OF BEGINNING
P.B.L. = POINT OF BEGINNING
S = CENTERLINE
N.B. & B.S.P. = NORTH & SOUTH POINT
V.V. = VERTICAL VERTICALLY
ESMT. = EASEMENT
DRAIN = DRAINAGE
UTL. = UTILITY
CL.F.C. = CONCRETE BLOCK
V.S.P.C. = VERTICAL SURFACE
C.B. = CONCRETE BLOCK
P.C. = POINT OF CURVATURE
P.T. = POINT OF TANGENCY
DESC. = DESCRIPTION
L = LENGTH
B = BEARING
C.B. = CORNER BEARING

LEGEND -
P.S.L. = POINT ON LINE
TYP. = TYPICAL
P.R.C. = POINT OF REVERSE CURVATURE
P.C.C. = POINT OF CURVATURE
P.A.B. = POINT OF BEGINNING
N.B. = NORTH BEARING
V.P. = VERTICAL POINT
CALC. = CALCULATED
P.A.M. = PERMANENT REFERENCE MONUMENT
F.F. = FINISHED FLOOR ELEVATION
B.S.L. = BUILDING SETBACK LINE
B.M. = BENCHMARK
B.B. = BACK BEARING

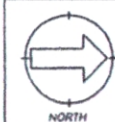

THIS BUILDING/PROPERTY DOES NOT LIE WITHIN
THE ESTABLISHED 100 YEAR FLOOD PLANE AS PER "FORM"
ZONE "A" MAP # 12089C 0555 E (12-18-2012)

5400 E. COLONIAL DR. ORLANDO, FL 32807 (407)-277-3232 FAX (407)-658-1436

NOTES:
1. THE UNDERSIGNED DOES HEREBY CERTIFY THAT THIS SURVEY MEETS THE STANDARDS OF PRACTICE SET FORTH BY THE FLORIDA BOARD OF PROFESSIONAL SURVEYORS AND MAPPERS IN CHAPTER 54-17 FLORIDA ADMINISTRATIVE CODE PURSUANT TO SECTION 472.027, FLORIDA STATUTES.
2. UNLESS ENDORSED WITH SURVEYOR'S SIGNATURE AND ORIGINAL BASED SEAL, THIS SURVEY MAP OR COPIES ARE NOT VALID.
3. THIS SURVEY HAS BEEN PREPARED FROM TELE INFORMATION FURNISHED TO THE SURVEYOR. THERE MAY BE OTHER RESTRICTIONS OR EASEMENTS THAT AFFECT THIS PROPERTY.
4. NO UNDERGROUND IMPROVEMENTS HAVE BEEN LOCATED UNLESS OTHERWISE SHOWN.
5. THIS SURVEY IS PREPARED FOR THE SOLE BENEFIT OF THOSE CERTIFIED TO AND SHOULD NOT BE RELIED UPON BY ANY OTHER ENTITY.
6. DIMENSIONS SHOWN FOR THE LOCATION OF IMPROVEMENTS HEREON SHOULD NOT BE USED TO RECONSTRUCT BOUNDARY LINES.
7. BEARINGS, ARE BASED ASSUMED DATUM AND ON THE LINE SHOWN AS BASE BEARING (B.B.).
8. ELEVATIONS, IF SHOWN, ARE BASED ON NORTH AMERICAN VERTICAL DATUM OF 1986, UNLESS OTHERWISE NOTED.
9. CERTIFICATE OF AUTHORIZATION NO. 4086

CERTIFIED BY:

James W. Scott
JAMES W. SCOTT, R.L.S. # 4714
JAMES W. SCOTT, R.L.S. # 4801

SCALE 1" = 20' DRAWN BY: N/E
DATE: PLOT PLAN 03-11-2024
ORDER NO. 24-2458